
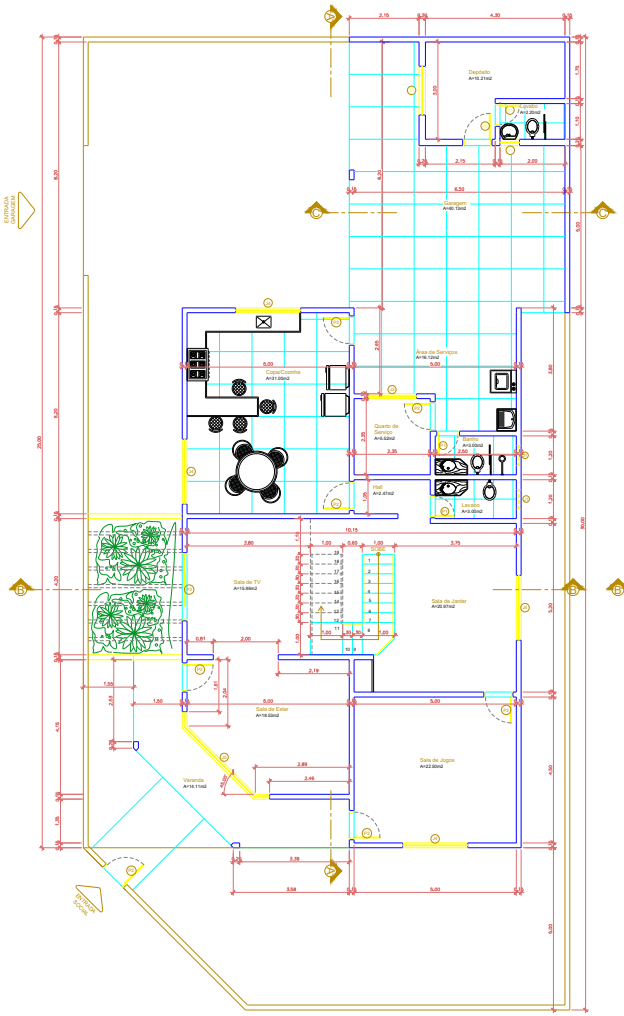


PLANTA BAIXA - TÉRREO


ESCALA 1:50

ESQUADRIAS	
PORTAS	
Código	Medida
P1	0.60 x 2.10
P2	0.80 x 2.10
P3	2.00 x 2.10
JANELAS	
Código	Medida
J1	0.60 x 0.50
J2	1.00 x 0.50
J3	1.50 x 1.20
J4	2.00 x 1.20
J5	4.00 x 1.20

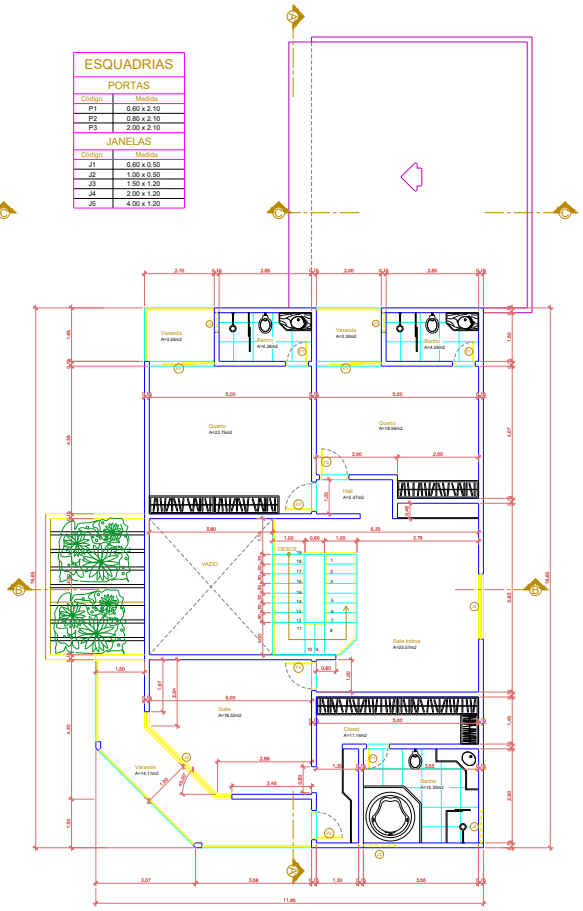


PLANTA BAIXA - SUPERIOR

ESCALA 1:50

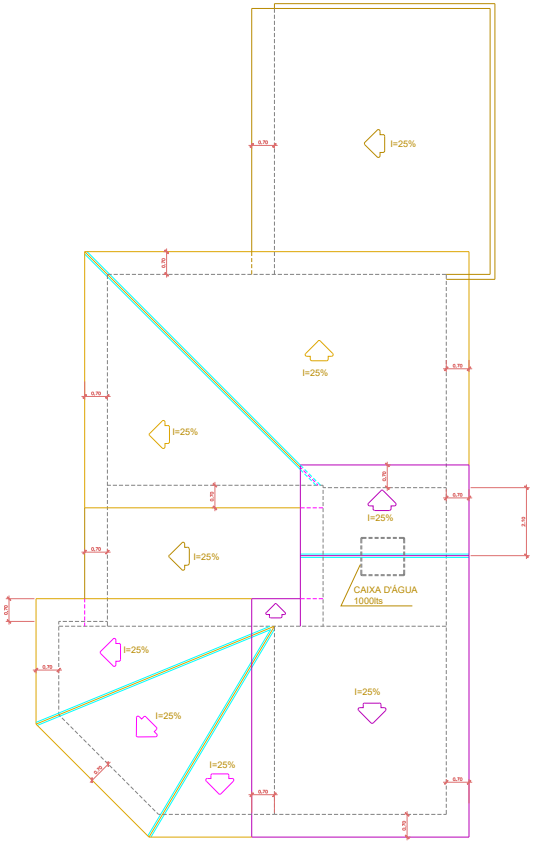

PLANTA DE COBERTURA

ESCALA 1:50

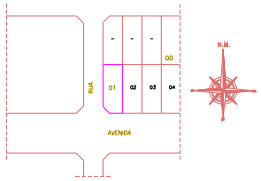

PLANTA DE SITUAÇÃO

SEM ESCALA

Aprovações:

PROJETO RESIDENCIAL
ARQUITETURA

Local:
-

Proprietário:
-

Autor do Projeto:
-

Responsável Técnico:
-

Áreas:
TERRENO: 437.00m2
TÉRREO: 235.22m2
SUPERIOR: 153.67m2
TOTAL A CONSTRUIR: 388.89m2

Conteúdo:
PLANTA BAIXA - TÉRREO E SUPERIOR.
PLANTA DE COBERTURA.
PLANTA DE SITUAÇÃO

Desenho:
www.addhouse.com

Data:

Escalas:
INDICADAS

Folha:
01/02